


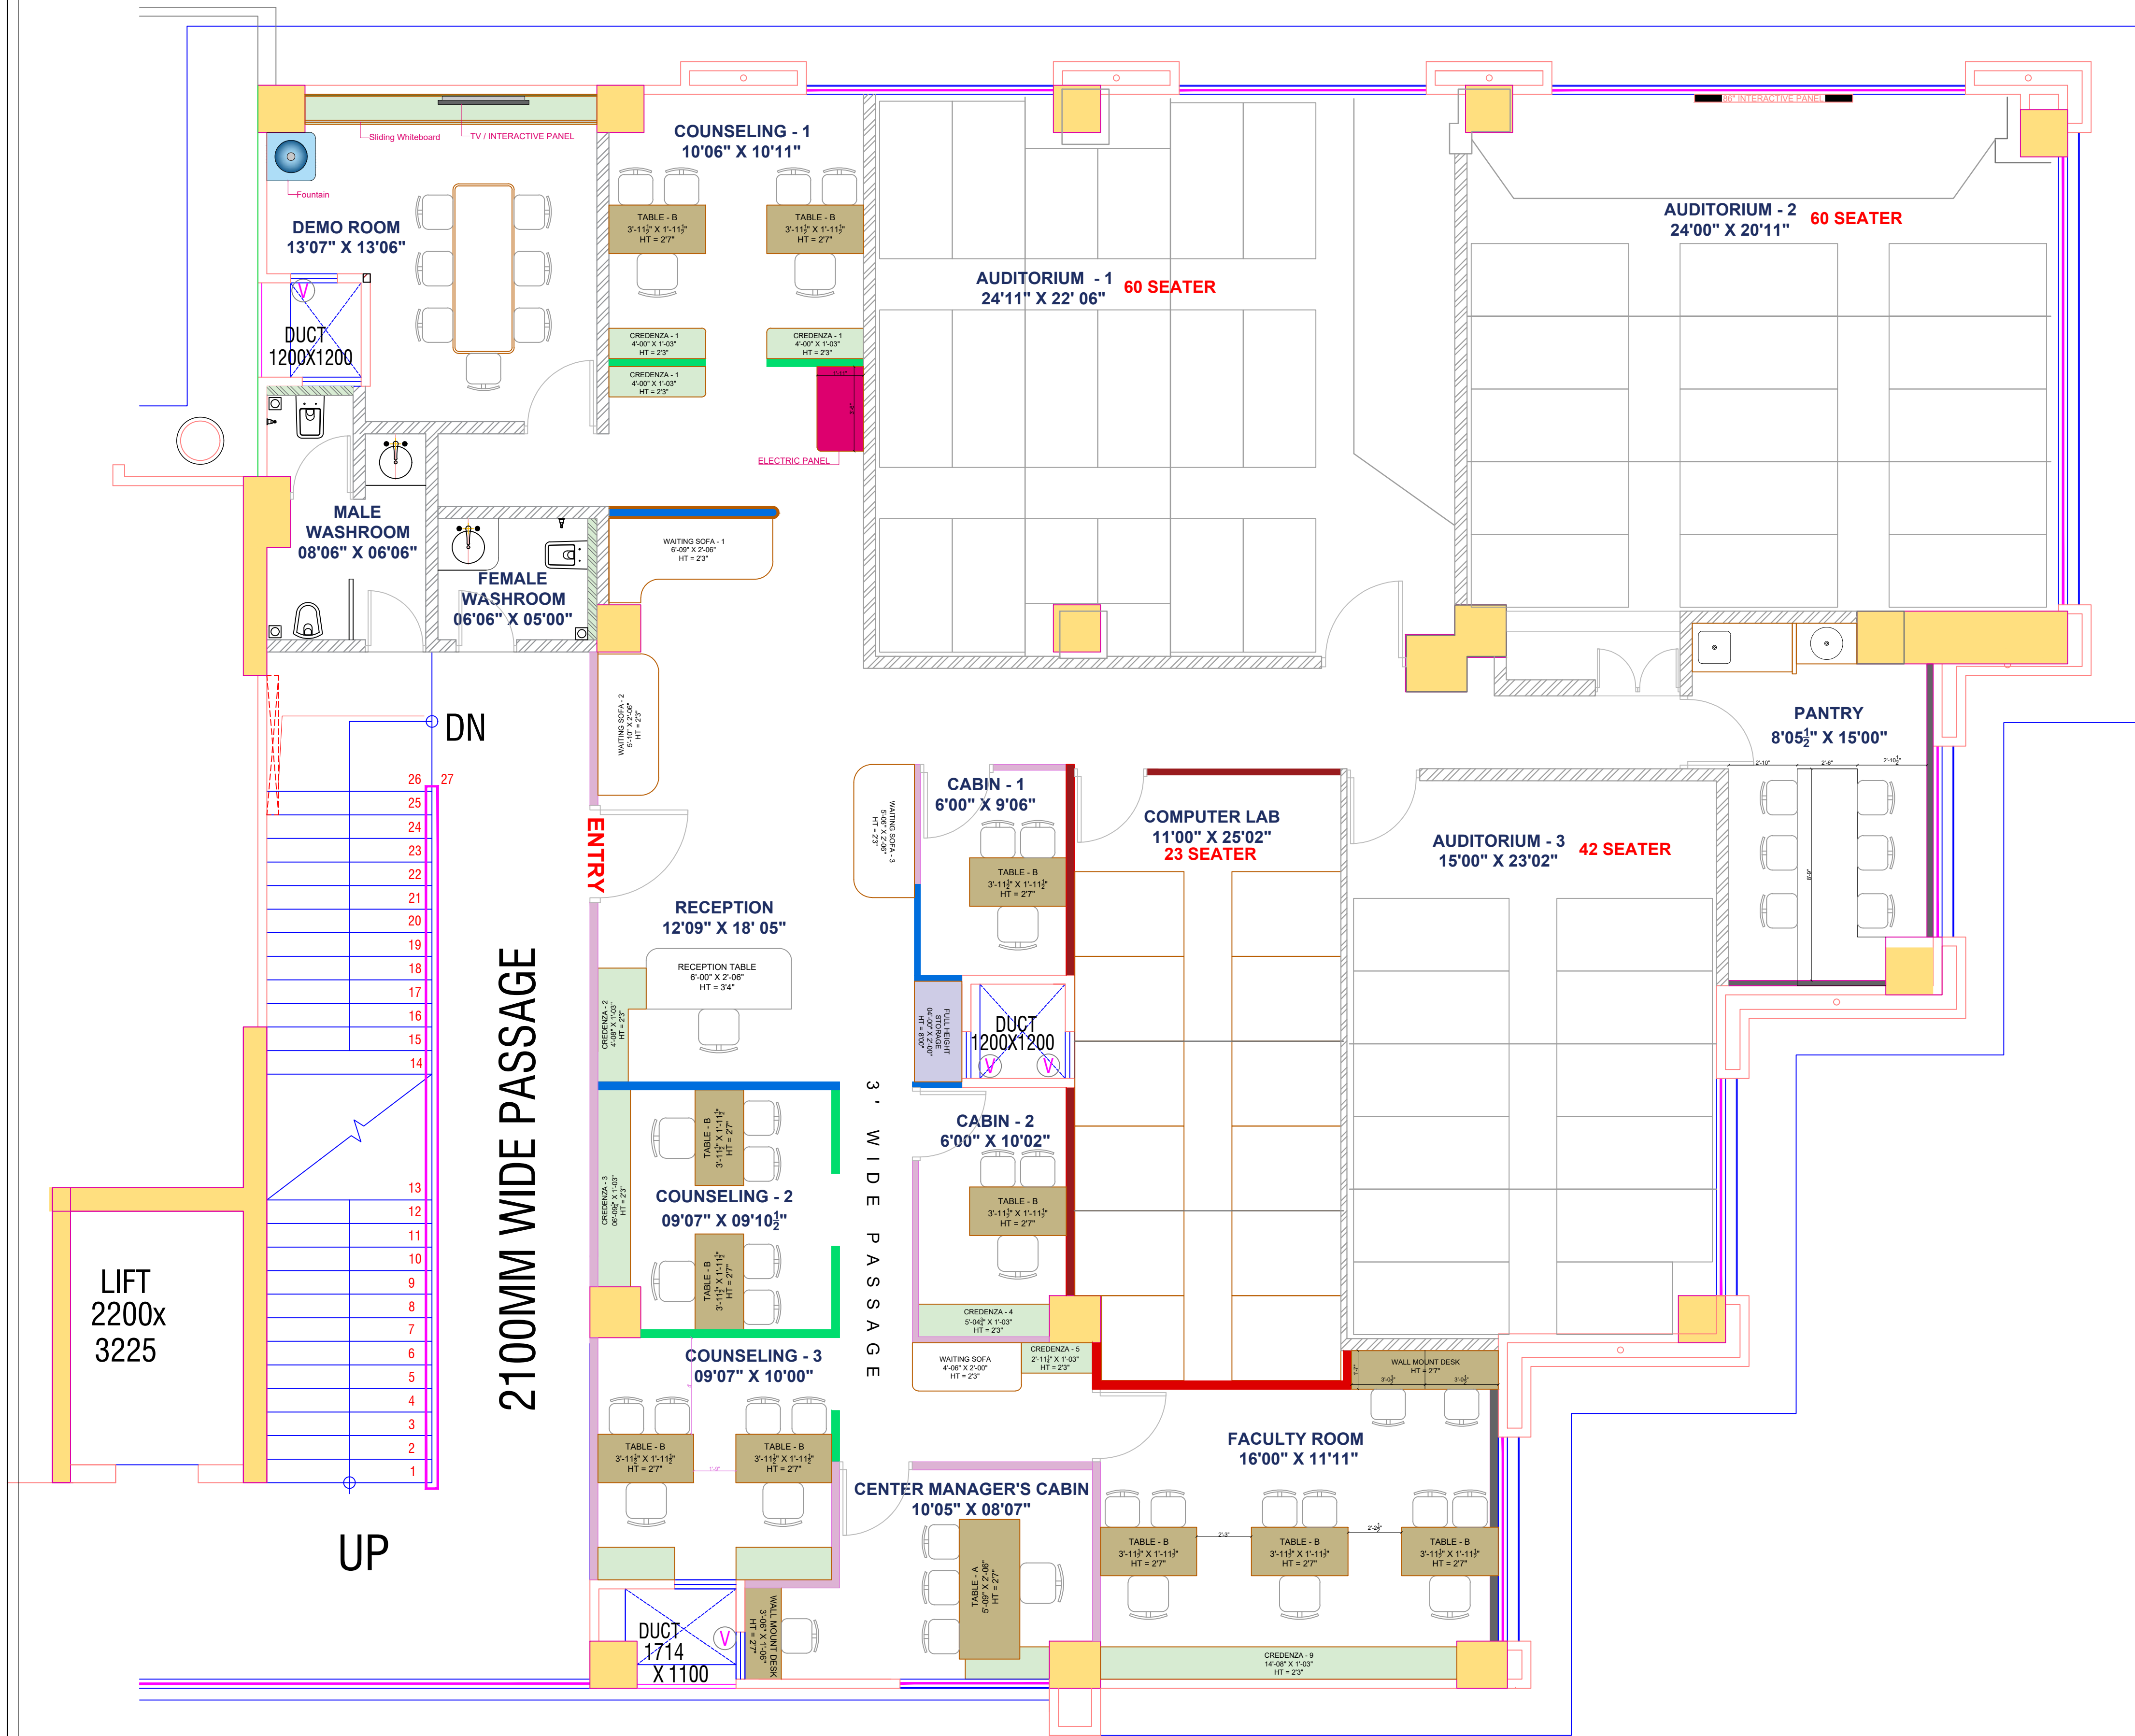

PROJECT

ISCON JANMAHAAL

OFFICE AND COACHING

N

E

SHEET NO.

01

CLIENT NAME

MANISH SHAH - MD

DESCRIPTION

FLOOR PLAN LAYOUT

DRAWING NO.

01

DATE

04-01-2025

SCALE

NTS

REVISION

07

DRN BY: ANJLI ZALA

CHKD BY:

NOTES :

•

DRG. SHALL NOT BE SCALED, ONLY WRITTEN DIMENSION ARE FOLLOWED.

•

ALL DIMENSION ARE IN FEET & INCH.

•

THIS DRG. IS NOT USE FOR GOVERNMENT WORK.

•

IF ANY CHANGE OR QUERY PLEASE INFORM US OTHERWISE WE ARE NOT RESPONSIBLE FOR ANY FAULT.

•

THIS DRG. DRAWN BY CLIENT REQUIREMENT AND THEIR RESPONSIBILITY.

•

ANY DISCREPENCY IN THE DRAWING TO BE BROUGHT IN THE DESIGNER'S NOTICE BEFORE EXECUTION ON SITE.

OWNER'S SIGN :

AREA :3600 Sq.ft

SYMBOL	DETAILS
	MASONRY WALL
	SOUND PROOF PARTITION (Till the ceiling)
	SOUND PROOF PARTITION (4'6" SOLID THAN GLASS UPTO CEILING)
	PARTITION (3'6" SOLID THAN GLASS UPTO CEILING)
	HALF PARTITION (3'6" HEIGHT)